PRODUCED BY AN AUTODESK STUDENT VERSION

SHEET NO.1 OF 16

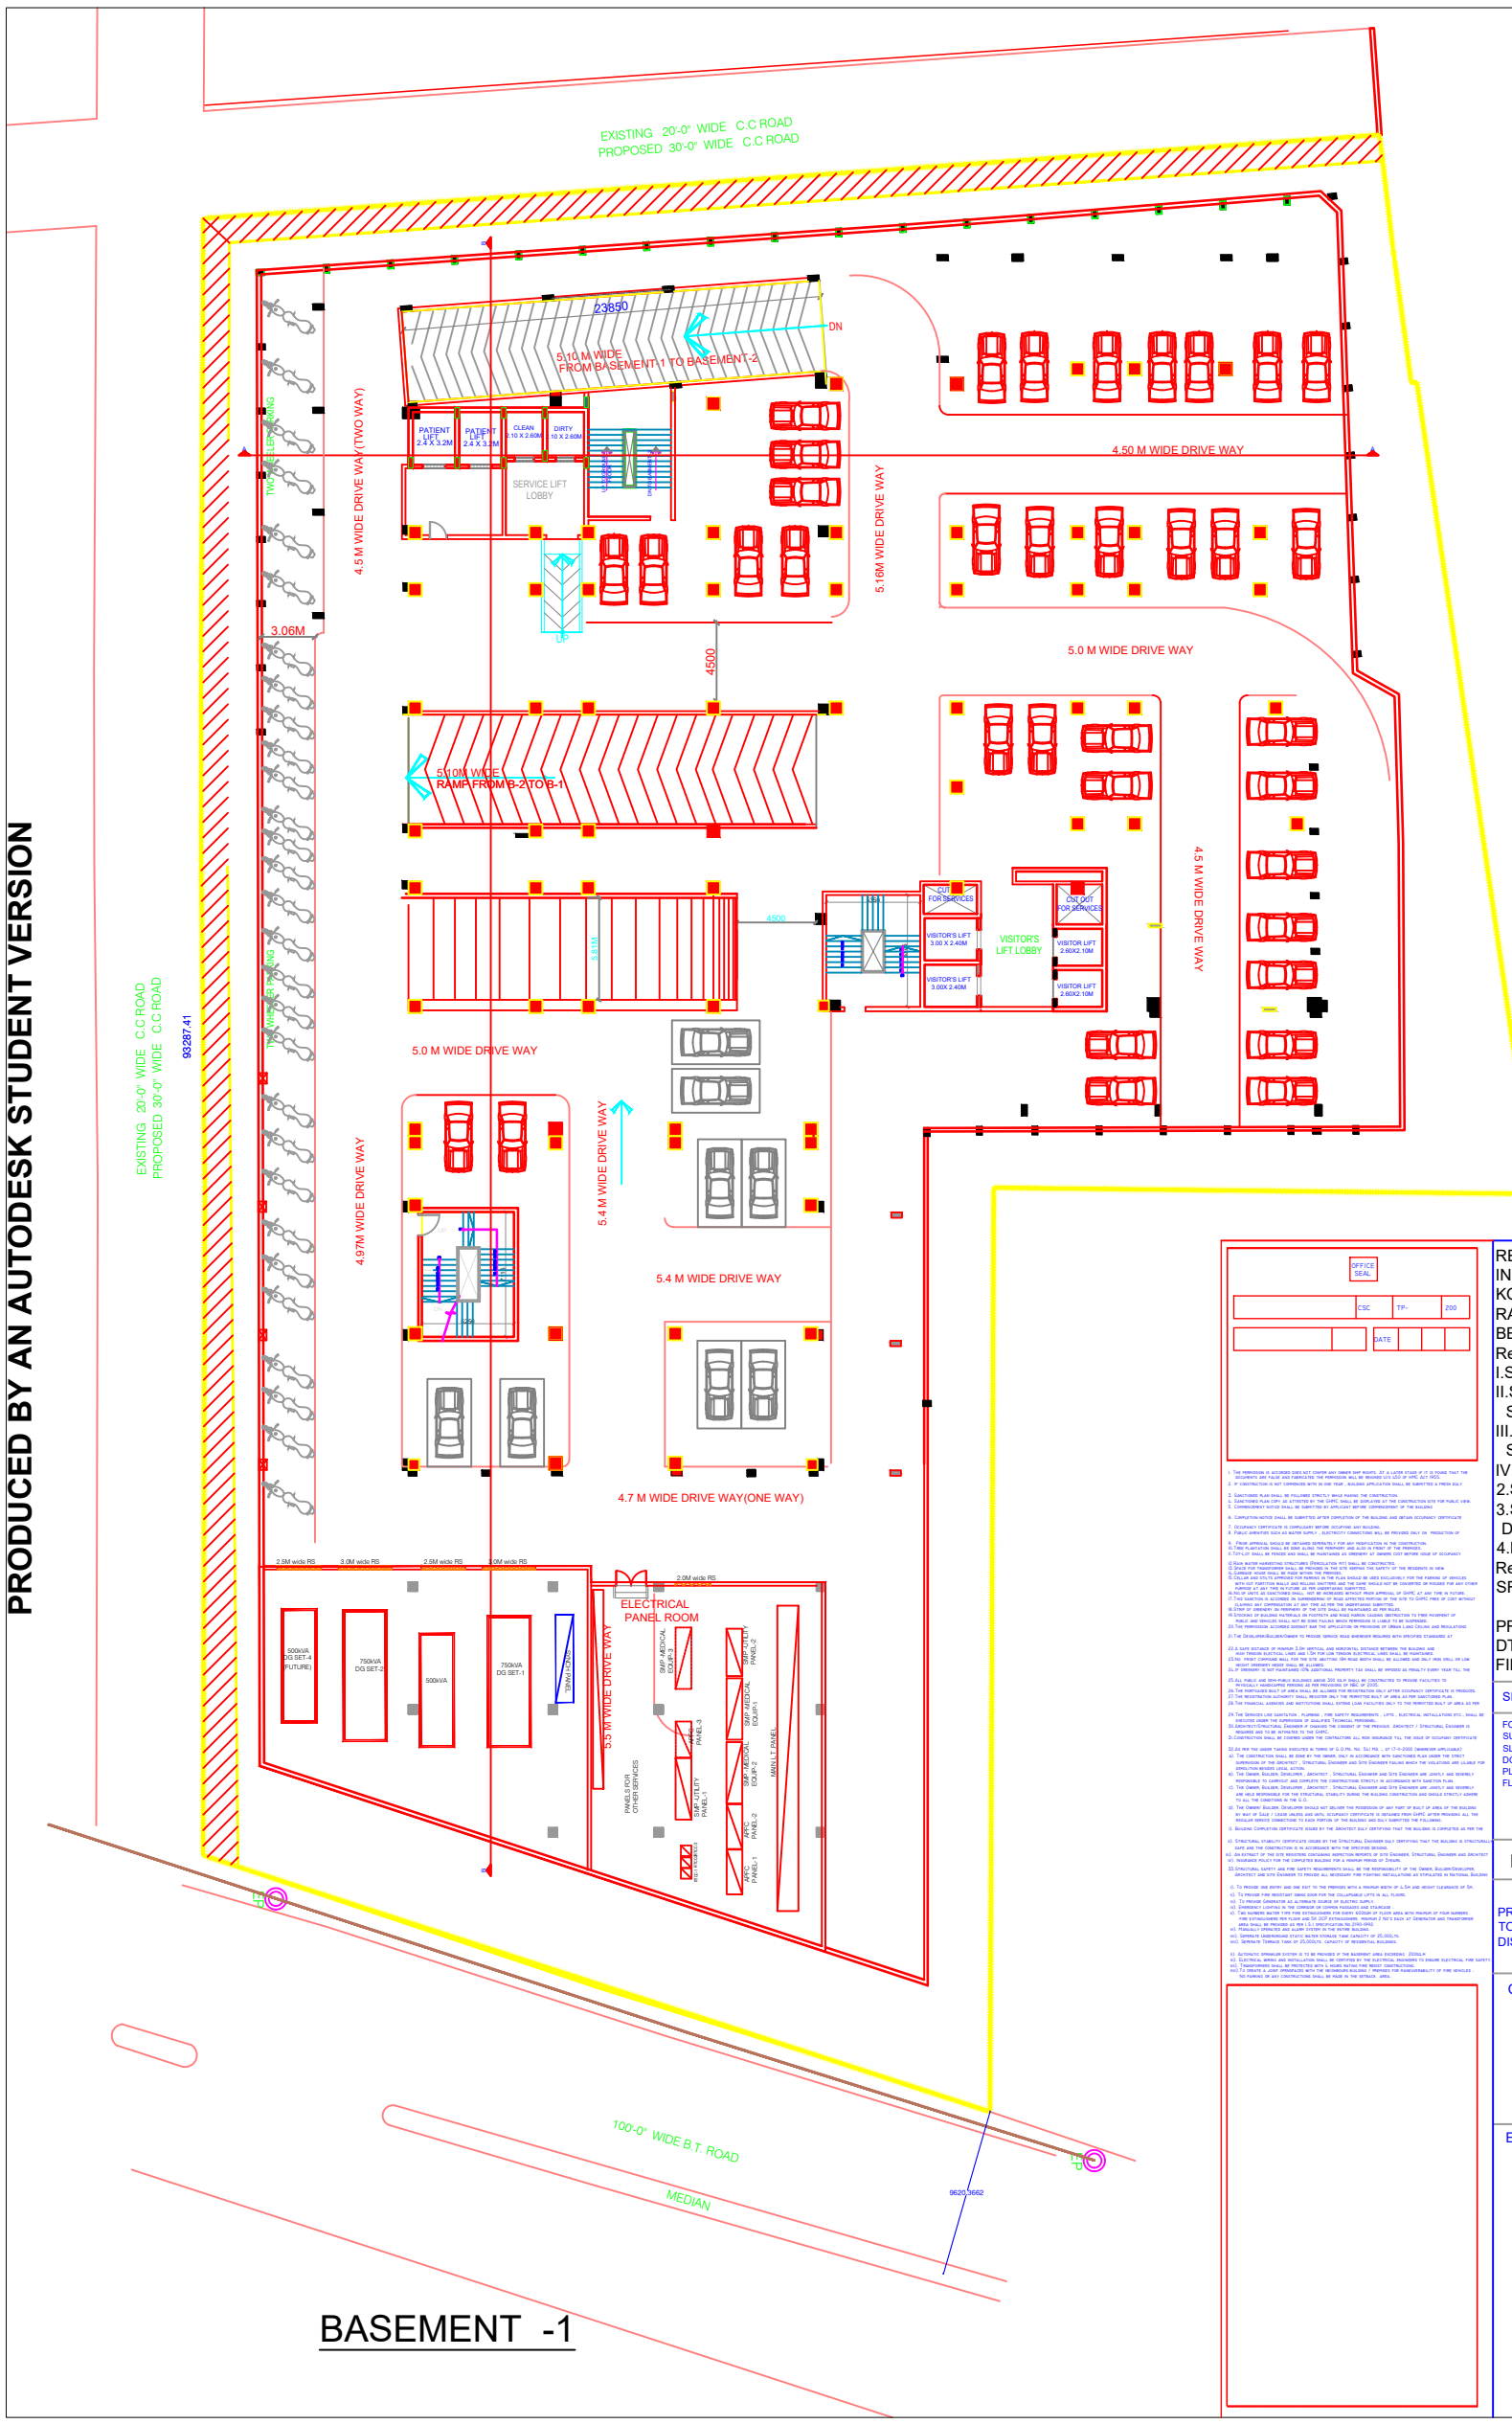

BASEMENT -1

OFFICE SEAL

	CSC	TP-	200
		DATE	

1. THE PERMISSION IS ACCORDED DOES NOT CONFER ANY OWNER OWN RIGHTS. AT A LATER STAGE IF IT IS FOUND THAT THE DOCUMENTS ARE FALSE AND FABRICATED THE PERMISSION WILL BE REVOKED U/S 12(3 OF HMC ACT 1955.
2. IF CONSTRUCTION IS NOT COMMENCED WITH IN ONE YEAR , BUILDING APPLICATION SHALL BE SUBMITTED A FRESH DULY
3. SANCTIONED PLAN SHALL BE FOLLOWED STRICTLY WHILE MAKING THE CONSTRUCTION.
4. SANCTIONED PLAN COPY AS ATTESTED BY THE GHMC SHALL BE DISPLAYED AT THE CONSTRUCTION SITE FOR PUBLIC VIEW.
5. COMMENCEMENT NOTICE SHALL BE SUBMITTED BY APPLICANT BEFORE COMMENCEMENT OF THE BUILDING.
6. COMPLETION NOTICE SHALL BE SUBMITTED AFTER COMPLETION OF THE BUILDING AND OBTAIN OCCUPANCY CERTIFICATE
7. OCCUPANCY CERTIFICATE IS COMPULSORY BEFORE OCCUPYING ANY BUILDING.
8. PUBLIC AMENITIES SUCH AS WATER SUPPLY , ELECTRICITY CONNECTIONS WILL BE PROVIDED ONLY ON PRODUCTION OF
9. FRESH APPROVAL SHOULD BE OBTAINED SEPERATELY FOR ANY MODIFICATION IN THE CONSTRUCTION.
10. TREE PLANTATION SHALL BE DONE ALONG THE PERIMAPH AND ALSO IN FRONT OF THE PREMISES.
11. TOT-LOT SHALL BE FENCED AND SHALL BE MAINTAINED AS OWENERY AT OWNERS COST BEFORE ISSUE OF OCCUPANCY
12. RAIN WATER HARVESTING STRUCTURES (PERCOLATION PIT) SHALL BE CONSTRUCTED.
13. SUFFICIENT WATER PRESSURE SHALL BE MAINTAINED TO THE TAPS WHICH INSURES THE SAFETY OF THE RESIDENTS IN VIEW.
14. GARBAGE HOUSE SHALL BE PLACE WITHIN THE PREMISES.
15. CELLAR AND STILTS APPROVED FOR PARKING IN THE PLAN SHOULD BE USED EXCLUSIVELY FOR THE PARKING OF VEHICLES . CELLAR AND STILTS SHOULD NOT BE CONVERTED OR PROVIDED FOR ANY OTHER PURPOSE AT ANY TIME IN FUTURE AS PER UNDERTAKING SUBMITTED.
16. NO.OF UNITS AS SANCTIONED SHALL NOT BE INCREASED WITHOUT PRIOR APPROVAL OF GHMC AT ANY TIME IN FUTURE
17. THIS SANCTION IS ACCORDED ON SURRENDERING OF ROAD AFFECTED PORTION OF THE SITE TO GHMC FREE OF COST WITHOUT CLAIMING ANY COMPENSATION AT ANY TIME AS PER THE UNDERTAKING SUBMITTED.
18. THE OWNERS/BUILDERS SHALL PLANT TREES ON THE ROAD MEDIAN AT THEIR OWN EXPENSE.
19. STOCKING OF BUILDING MATERIALS OR FOOTPATH AND ROAD PARKING CAUSING OBSTRUCTION TO FREE MOVEMENT OF PUBLIC AND VEHICLES SHALL NOT BE DONE FAILING WHICH PERMISSION IS LIABLE TO BE SUSPENDED.
20. THE PERMISSION ACCORDED DOESNOT BAR THE APPLICATION OR PROVISIONS OF URBAN LAND CEILING AND REGULATIONS
21. THE DEVELOPER/BUILDER/OWNER TO PROVIDE SERVICE ROAD WHEREVER REQUIRED WITH SPECIFIED STANDARDS AT
22. A SAFE DISTANCE OF MINIMUM 3.0M VERTICAL AND HORIZONTAL DISTANCE BETWEEN THE BUILDING AND HIGH TENSION ELECTRICAL LINES AND 1.5M FOR LOW TENSION ELECTRICAL LINES SHALL BE MAINTAINED.
23. NO FRONT COMPOUND WALL FOR THE SITE ABUTTING 18M ROAD WIDTH SHALL BE ALLOWED AND ONLY IRON GRILL OR LOW HEIGHT ORNEMENT HEDGE SHALL BE ALLOWED.
24. IF AMENENITY IS NOT MAINTAINED 10% ADDITIONAL PROPERTY TAX SHALL BE IMPOSED AS PENALTY EVERY YEAR TILL THE
25. ALL PUBLIC AND SEMI-PUBLIC BUILDINGS ABOVE 300 SQ.M SHALL BE CONSTRUCTED TO PROVIDE FACILITIES TO PHYSICALLY HANDICAPPED PERSONS AS PER PROVISIONS OF NBC OF 2005.
26. THE MORTGAGED BUILT UP AREA SHALL BE ALLOWED FOR REGISTRATION ONLY AFTER OCCUPANCY CERTIFICATE IS PRODUCED.
27. THE REGISTRATION AUTHORITY SHALL REGISTER ONLY THE PERMITTED BUILT UP AREA AS PER SANCTIONED PLAN.
28. THE FINANCIAL AGENCIES AND INSTITUTIONS SHALL EXTEND LOAN FACILITIES ONLY TO THE PERMITTED BUILT UP AREA AS PER
29. THE SERVICES LIKE SANITATION , PLUMBING , FIRE SAFETY REQUIREMENTS , LIFTS , ELECTRICAL INSTALLATIONS ETC., SHALL BE EXECUTED UNDER THE SUPERVISION OF QUALIFIED TECHNICAL PERSONNEL.
30. ARCHITECT/STRUCTURAL ENGINEER IF CHANGED THE CONSENT OF THE PREVIOUS ARCHITECT / STRUCTURAL ENGINEER IS REQUIRED AND TO BE INTIMATED TO THE GHMC.
31. CONSTRUCTION SHALL BE COVERED UNDER THE CONTRACTORS ALL RISK INSURANCE TILL THE ISSUE OF OCCUPANCY CERTIFICATE
32. AS PER THE UNDER TAKING EXECUTED IN FORM OF G.O.MS. NO. 52,I.MA , dt:-21-2-2005 (WHEREVER APPLICABLE)
A). THE CONSTRUCTION SHALL BE DONE BY THE OWNER, ONLY IN ACCORDANCE WITH SANCTIONED PLAN UNDER THE STRICT SUPERVISION OF THE ARCHITECT , STRUCTURAL ENGINEER AND SITE ENGINEER FAILING WHICH THE VIOLATIONS ARE LIABLE FOR DEMOLITION BESIDES LEGAL ACTION.
B). THE OWNER, BUILDER, DEVELOPER , ARCHITECT , STRUCTURAL ENGINEER AND SITE ENGINEER ARE JOINTLY AND SEVERELY RESPONSIBLE TO CARRYOUT AND COMPLETE THE CONSTRUCTIONS STRICTLY IN ACCORDANCE WITH SANCTION PLAN.
C). THE OWNER, BUILDER, DEVELOPER , ARCHITECT , STRUCTURAL ENGINEER AND SITE ENGINEER ARE JOINTLY AND SEVERELY ARE HELD RESPONSIBLE FOR THE STRUCTURAL STABILITY DURING THE BUILDING CONSTRUCTION AND SHOULD STRICTLY ADHERE TO ALL THE CONDITIONS IN THE G.O.
D). THE OWNER/ BUILDER, DEVELOPER SHOULD NOT DELIVER THE POSSESSION OF ANY PART OF BUILT UP AREA OF THE BUILDING BY WAY OF SALE / LEASE UNLESS AND UNTIL OCCUPANCY CERTIFICATE IS OBTAINED FROM GHMC AFTER PROVIDING ALL THE REGULAR SERVICE CONNECTIONS TO EACH PORTION OF THE BUILDING AND DULY SUBMITTED THE FOLLOWING.
i). BUILDING COMPLETION CERTIFICATE ISSUED BY THE ARCHITECT DULY CERTIFYING THAT THE BUILDING IS COMPLETED AS PER THE
ii). STRUCTURAL STABILITY CERTIFICATE ISSUED BY THE STRUCTURAL ENGINEER DULY CERTIFYING THAT THE BUILDING IS STRUCTURALLY SAFE AND THE CONSTRUCTION IS IN ACCORDANCE WITH THE SPECIFIED DESIGNS.
iii). AN EXTRACT OF THE SITE REGISTERS CONTAINING INSPECTION REPORTS OF SITE ENGINEER, STRUCTURAL ENGINEER AND ARCHITECT
iv). INSURANCE POLICY FOR THE COMPLETED BUILDING FOR A MINIMUM PERIOD OF 3YEARS.
33. STRUCTURAL SAFETY AND FIRE SAFETY REQUIREMENTS SHALL BE THE RESPONSIBILITY OF THE OWNER, BUILDER,DEVELOPER, ARCHITECT AND SITE ENGINEER TO PROVIDE ALL NECESSARY FIRE FIGHTING INSTALLATIONS AS STIPULATED IN NATIONAL BUILDING
i). TO PROVIDE ONE ENTRY AND ONE EXIT TO THE PREMISES WITH A MINIMUM WIDTH OF 4.5M AND HEIGHT CLEARANCE OF 5M.
ii). TO PROVIDE FIRE RESISTANT SWING DOOR FOR THE COLLAPSIABLE LIFTS IN ALL FLOORS.
iii). TO PROVIDE GENERATOR AS ALTERNATE SOURCE OF ELECTRIC SUPPLY.
iv). EMERGENCY LIGHTING IN THE CORRIDOR OR COMMON PASSAGES AND STAIRCASE .
v). TWO NUMBERS WATER TYPE FIRE EXTINGUISHERS FOR EVERY 500SQM OF FLOOR AREA WITH MINIMUM OF FOUR NUMBERS FIRE EXTINGUISHERS PER FLOOR AND 5K DCP EXTINGUISHERS MINIMUM 2 NOS EACH AT GENERATOR AND TRANSFORMER AREA SHALL BE PROVIDED AS PER I.S.I SPECIFICATION NO.2190-1992.
vi). SEPARATE UNDERGROUND STATIC WATER STORAGE TANK CAPACITY OF 25,000LTS.
vii). SEPARATE UNDERGROUND STATIC WATER STORAGE TANK CAPACITY OF 25,000LTS.
viii). SEPARATE TERRACE TANK OF 25,000LTS. CAPACITY OF RESIDENTIAL BUILDINGS.
x). AUTOMATIC SPRINKLER SYSTEM IS TO BE PROVIDED IF THE BASEMENT AREA EXCEEDS 200SQ.M
xi). ELECTRICAL WIRING AND INSTALLATION SHALL BE CERTIFIED BY THE ELECTRICAL ENGINEERS TO ENSURE ELECTRICAL FIRE SAFETY
xii). TRANSFORMERS SHALL BE PROTECTED WITH 4 HOURS RATING FIRE RESIST CONSTRUCTIONS.
xiii). PARKING AREA SHOULD BE MADE FIRE PROOF AND SUFFICIENT ARRANGEMENTS FOR MANEUVERABILITY OF FIRE VEHICLES .
34. NO PARKING OR ANY CONSTRUCTIONS SHALL BE MADE IN THE SETBACK AREA.

REVISED PLAN OF PROPOSED HOSPITAL
IN PART OF SURVEY NO.12 (PART) SITUATED AT
KONDAPUR (V), SERI LINGAM PALLY (MANDAL) ,
RANGA REDDY DIST. - AP.
BELONGING TO M/s SREE CONSTRUCTIONS
Rep By its MANAGING DIRECTOR
I.SRI JAYATI BHAI PATEL S/o SRI POPAT BHAI
II.SRI MANSUKH BHAI PATEL S/O
SRI RANCHOD BHAI PATEL
III.SRI GHANSHYAM BHAI PATEL S/O
SRI ARJAN BHAI PATEL
IV.SRI MOHAN BHAI PATEL S/O SRI GANGDAS PATEL
2.SRI K.BABU RAO S/O Late K.V.NARASAIAH
3.SMT K.RANI W/O SRI K.BABU RAO
DEVELOPMENT AGREEMENT CUM G.P.A HOLDER
4.M/S LEGEND ESTATES PVT LTD.,
Rep By its MANAGING DIRECTOR
SRI B.NAGESWARA RAO S/O SRI B.CHENNAIAH

PREVIOUS PERMIT NO.1667/HO/WZ/COR-11/
DT02.04.2011
FILE NO. 016/CSC/TP-11/2008

SPECIFICATIONS		LEGEND OF OPENINGS	
FOUNDATION	R.C.C FOOTINGS	DOORS	D1 1.50 X 2.0M
SUPER STRUCTURE	B.K. IN CM		D2 1.00 X 2.0M
SLAB, COLUMNS	R.C.C		D3 0.90 X 2.0M
DOORS WINDOWS	C.T WOOD	WINDOWS	W1 2.0 X 1.2M
PLASTERING	C.M. IN 1:6		W2 1.5 X 1.2M
FLOORING	MOSAIC		W3 1.5X 0.9M
			W4 0.9X 1.2M
		VENTILATOR	V 0.9 X 0.45M

REFERENCES

PROPOSED TO BE DISMANTLED — EXISTING — SCALE 1: 100 M

NORTH

OWNERS SIGNATURE

BUILDERS SIGNATURE

BL/226/07

ENGINEER SIGNATURE

ARCHITECT SIGNATURE

PRODUCED BY AN AUTODESK STUDENT VERSION